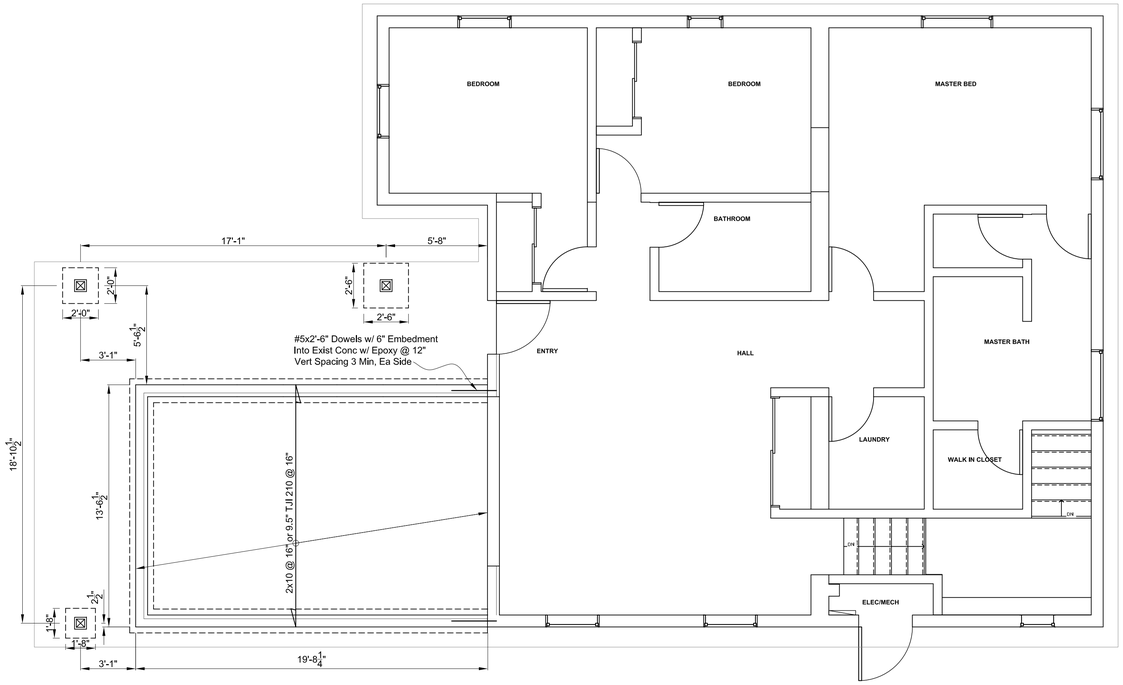

1 1st Floor Framing & Fdn Plan for Addition
1/4"=1'-0"

Feet 0 1 2 3 4 5 6 7 8 9 10 11 12

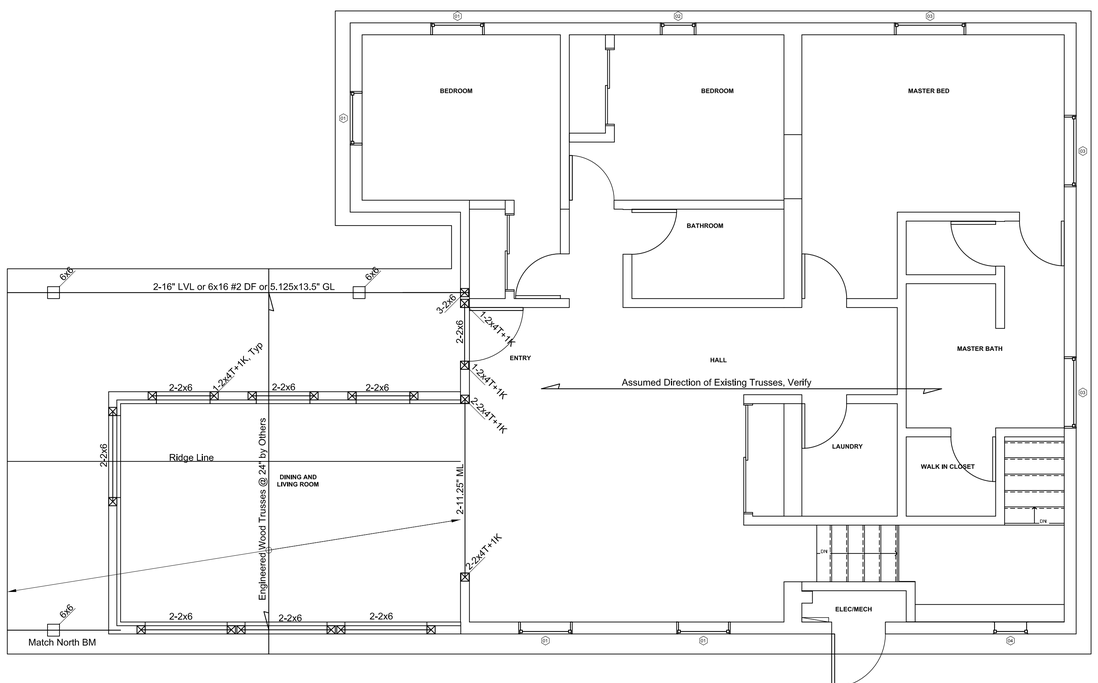

2 Roof Framing Plan for Addition
1/4"=1'-0"

Feet 0 1 2 3 4 5 6 7 8 9 10 11 12

Contractor to verify all dimensions, elevations and construction as required.

Abbreviations:
B.O. = Bottom Of
Blk = Block
BM = Beam
Bott = Bottom
Btwn = Between
Cant = Cantilever
Col = Column
Clr = Clear
Conn = Connection
Conc = Concrete
Cont = Continuous
CSOG = Conc Slab on Grade
DF = Douglas Fir
DN = Down
Ea = Each
Exist = Existing
Fdn = Foundation
Ftg = Footing
FS = Far Side
Hdr = Header
Ht = Height
Jst = Joist
K = King Stud
Loc = Location
MAS = Masonry
Max = Maximum
Min = Minimum
ML = Microllam
NS = Near Side
OH = Opposite Hand
Opp = Opposite
OS = Outside
PAF = Power Actuated Fastener
PFA = Post From Above
PFA&B = Post From Above & to Below
PL = Plate
PT = Pressure Treated
Req'd = Required
Rdg = Ridge
RS = Rough Sawn (Full Dim)
RW = Redwood
Sim = Similar
Std = Standard
Stl = Steel
SYP = Southern Yellow Pine
T = Trimmer Stud
T&B = Top & Bottom
TBD = To Be Determined
TJI = Truss Joist, I Joist
T.O. = Top Of
Typ = Typical
UNO = Unless Noted Otherwise
WWF = Welded Wire Fabric

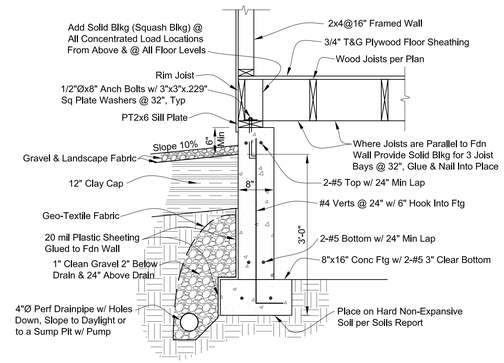

4 Fdn Section
3/4"=1'-0"

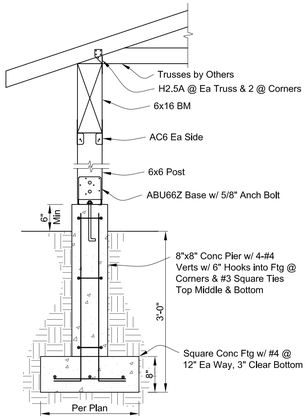

5 Fdn Section
3/4"=1'-0"

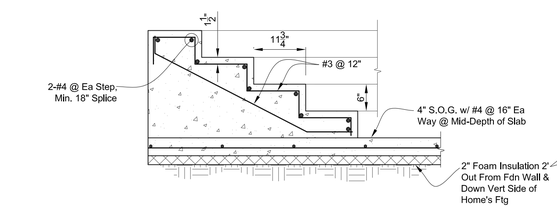

6 Sunken Patio Section
3/4"=1'-0"

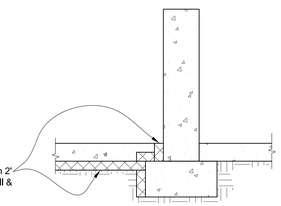

7 Frost Protected Shallow Fdn Section
3/4"=1'-0"

Design Criteria:
2015 IBC & IRC (2021 ICC)
Snow 30 psf
Floor LL 40 psf
Wind 142 mph V_{ult} Exp C
Wood Framing #2 Doug Fir
Concrete 4000 psi
Rebar 60,000 psi

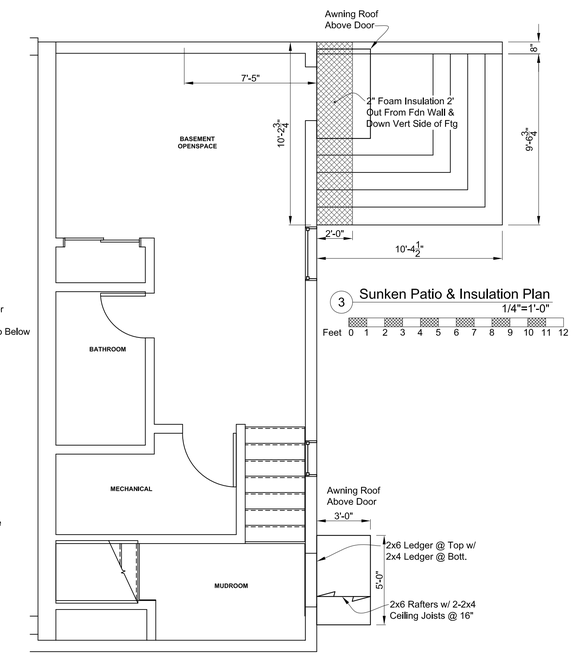

3 Sunken Patio & Insulation Plan
1/4"=1'-0"

Feet 0 1 2 3 4 5 6 7 8 9 10 11 12

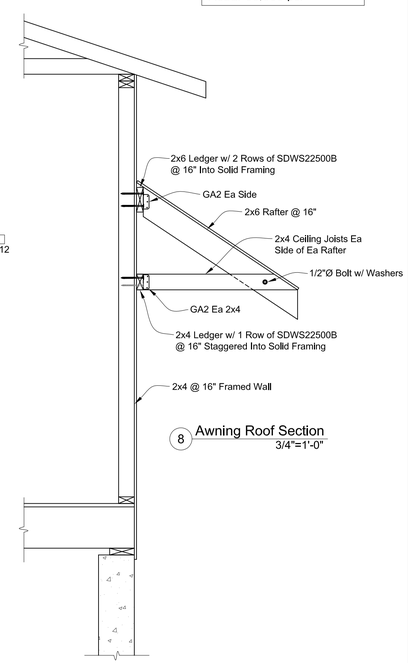

8 Awning Roof Section
3/4"=1'-0"

Lopez Smolens Associates
Consulting Architectural & Structural Engineers
3405 Penrose Place #104
Boulder, CO 80301
Office 303 447-2813
Fax 303 447-2814
www.LopezSmolensEngineers.com

The engineer and his consultants do not warrant or guarantee the accuracy and completeness of the work product herein beyond a reasonable diligence. If any mistakes, omissions or discrepencies are found to exist within the work product, the engineer shall be promptly notified so that he may have the opportunity to take whatever steps necessary to resolve them. Failure to promptly notify the engineer of such conditions shall absolve the engineer from any responsibility for the consequences of such discrepencies. Actions taken without the knowledge and consent of the engineer or in contradiction to the engineer's work product or recomendations shall become the responsibility not of the engineer, but of the parties responsible for taking such action.

Copyright Reserved

Jonathan Smolens
Digitally signed by Jonathan Smolens
Date: 2023.01.31 14:59:27 -07'00'
J22304
COLORADO LICENSED JONATHAN L. SMOLENS 38960 PROFESSIONAL ENGINEER
1/31/2023
Structural Only

Mark Rockwell Addition
275 Holbrook Street
Erie CO 80516

print date:	1/31/2023
drawn by:	JS
submittal:	
revision:	
project no:	J22304
sheet title:	Plans & Details
sheet no:	S1